SBUA - 2880 sft
West Facing

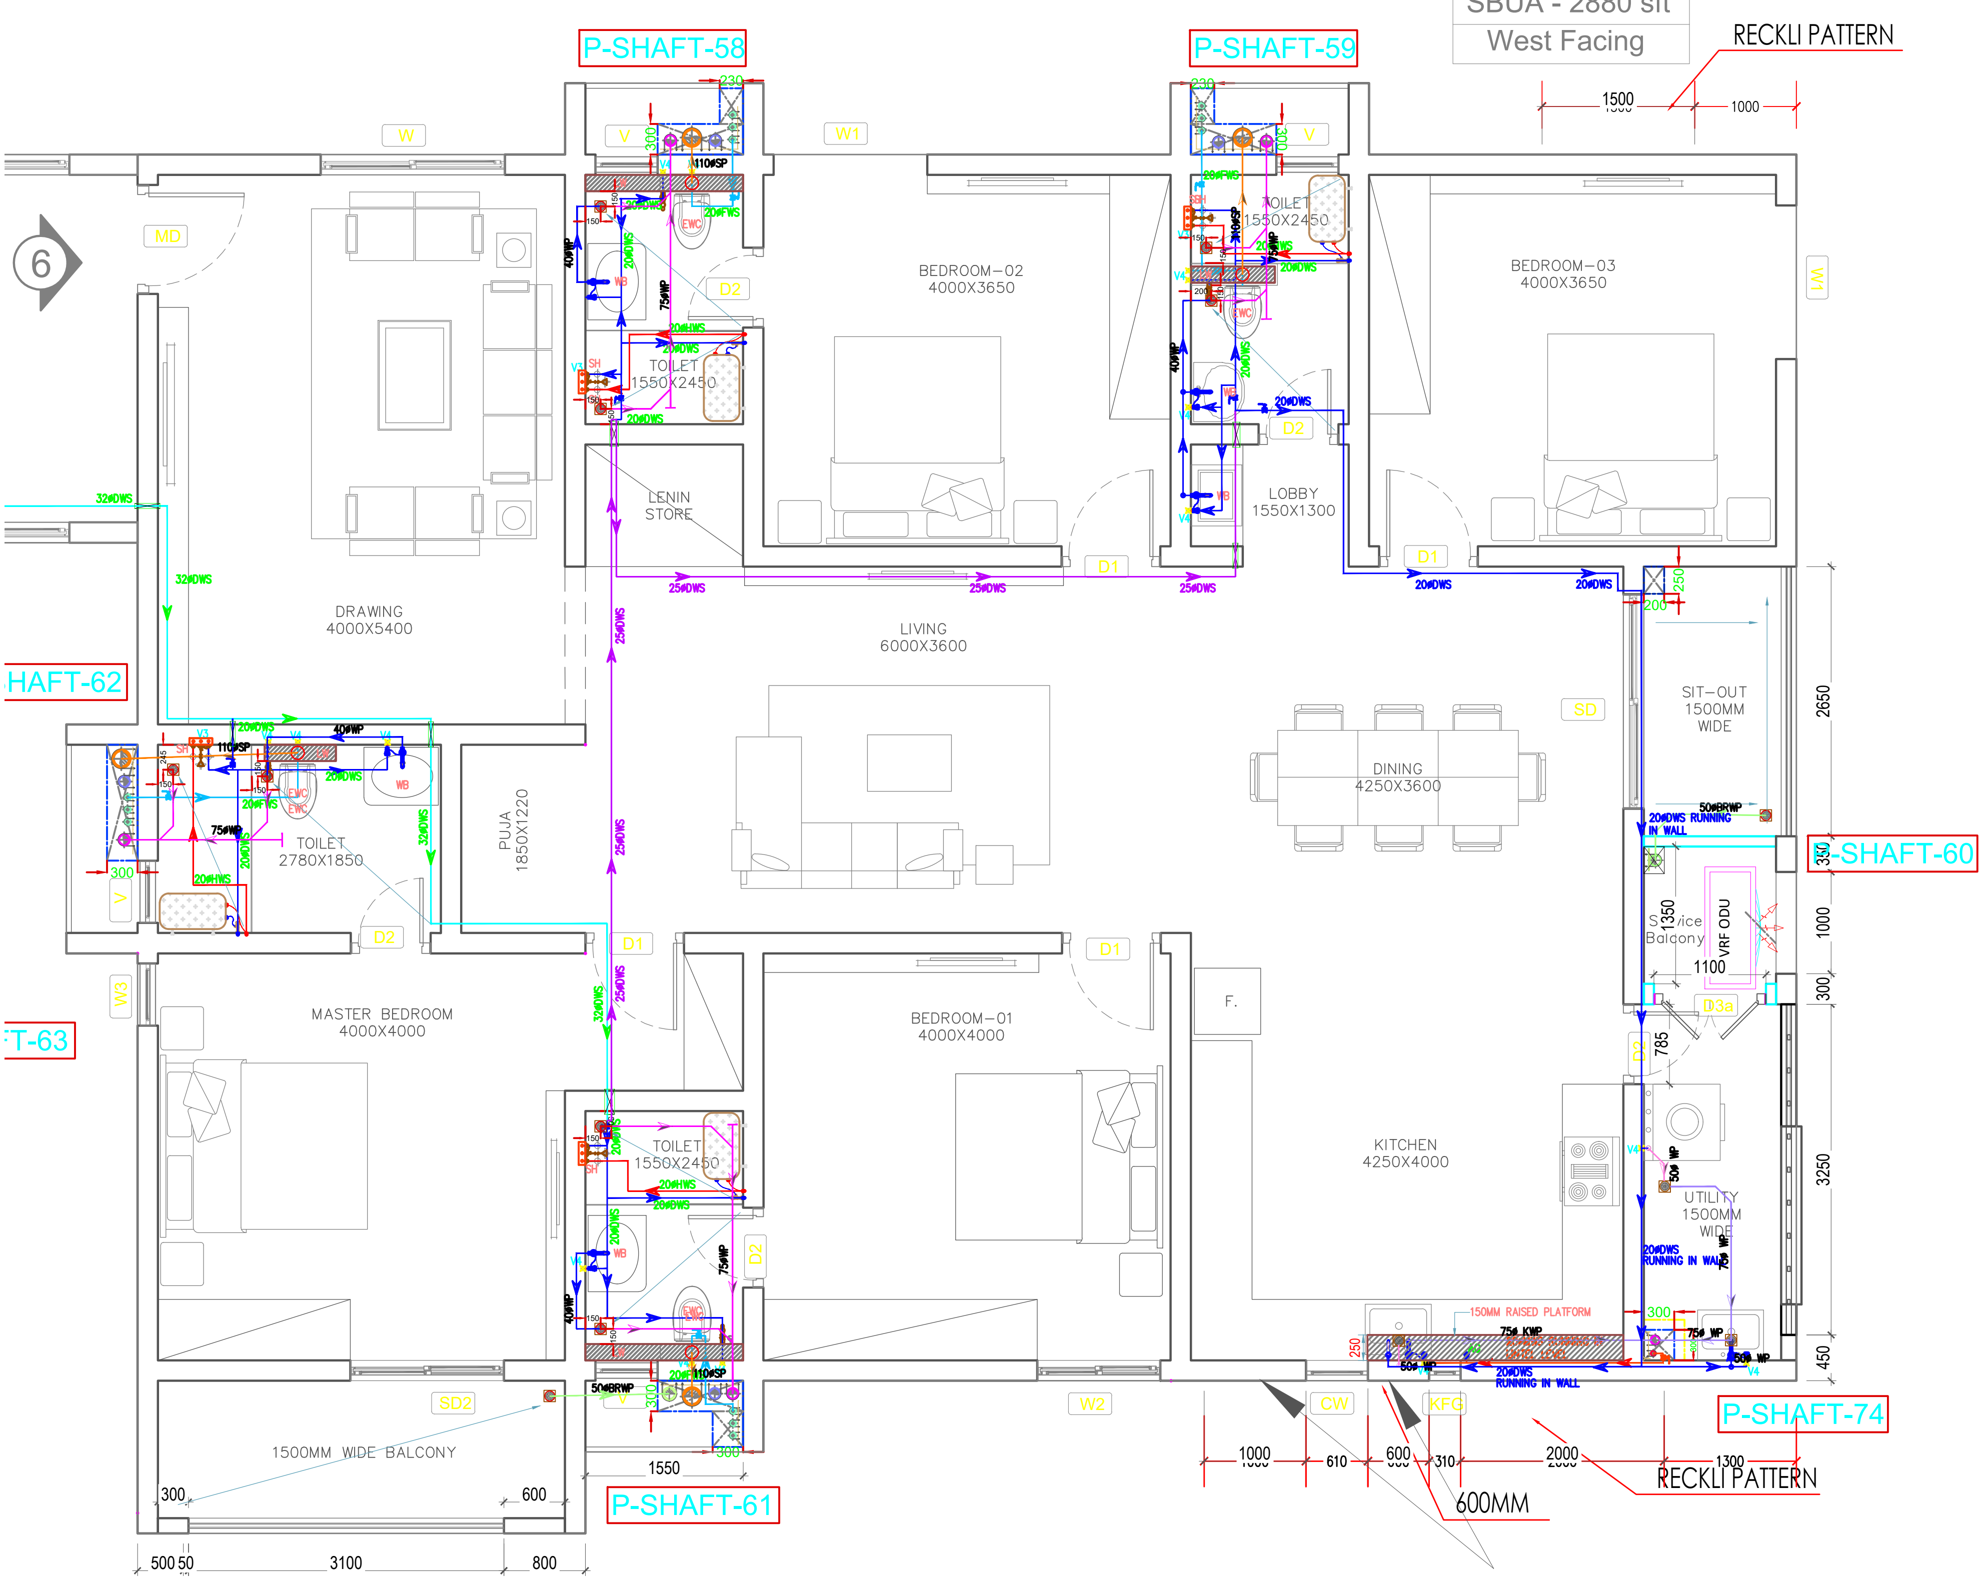

PLUMBING LEGEND :-

SYMBOL	DESCRIPTION
━━━	32mm DIA DWS PIPE
━━━	25mm DIA DWS PIPE
━━━	20mm DIA DWS PIPE
━━━	20mm DIA MWS PIPE
━━━	20mm DIA FWS PIPE
━━━	20mm DIA HWS PIPE
MW	32mm DIA WATER METER
➤➤➤➤	FLOW DIRECTION
━━━	110mm DIA SOIL PIPE
━━━	75mm DIA WASTE PIPE
━━━	75/50mm DIA BRW PIPE
━━━	40mm DIA WASTE PIPE
━━━	75mm DIA KITCHEN WASTE PIPE
━━━	50mm DIA UTILITY WASTE PIPE
	BALL VALVE
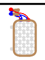	GEYSER
	FLOOR DRAIN
	SHOWER